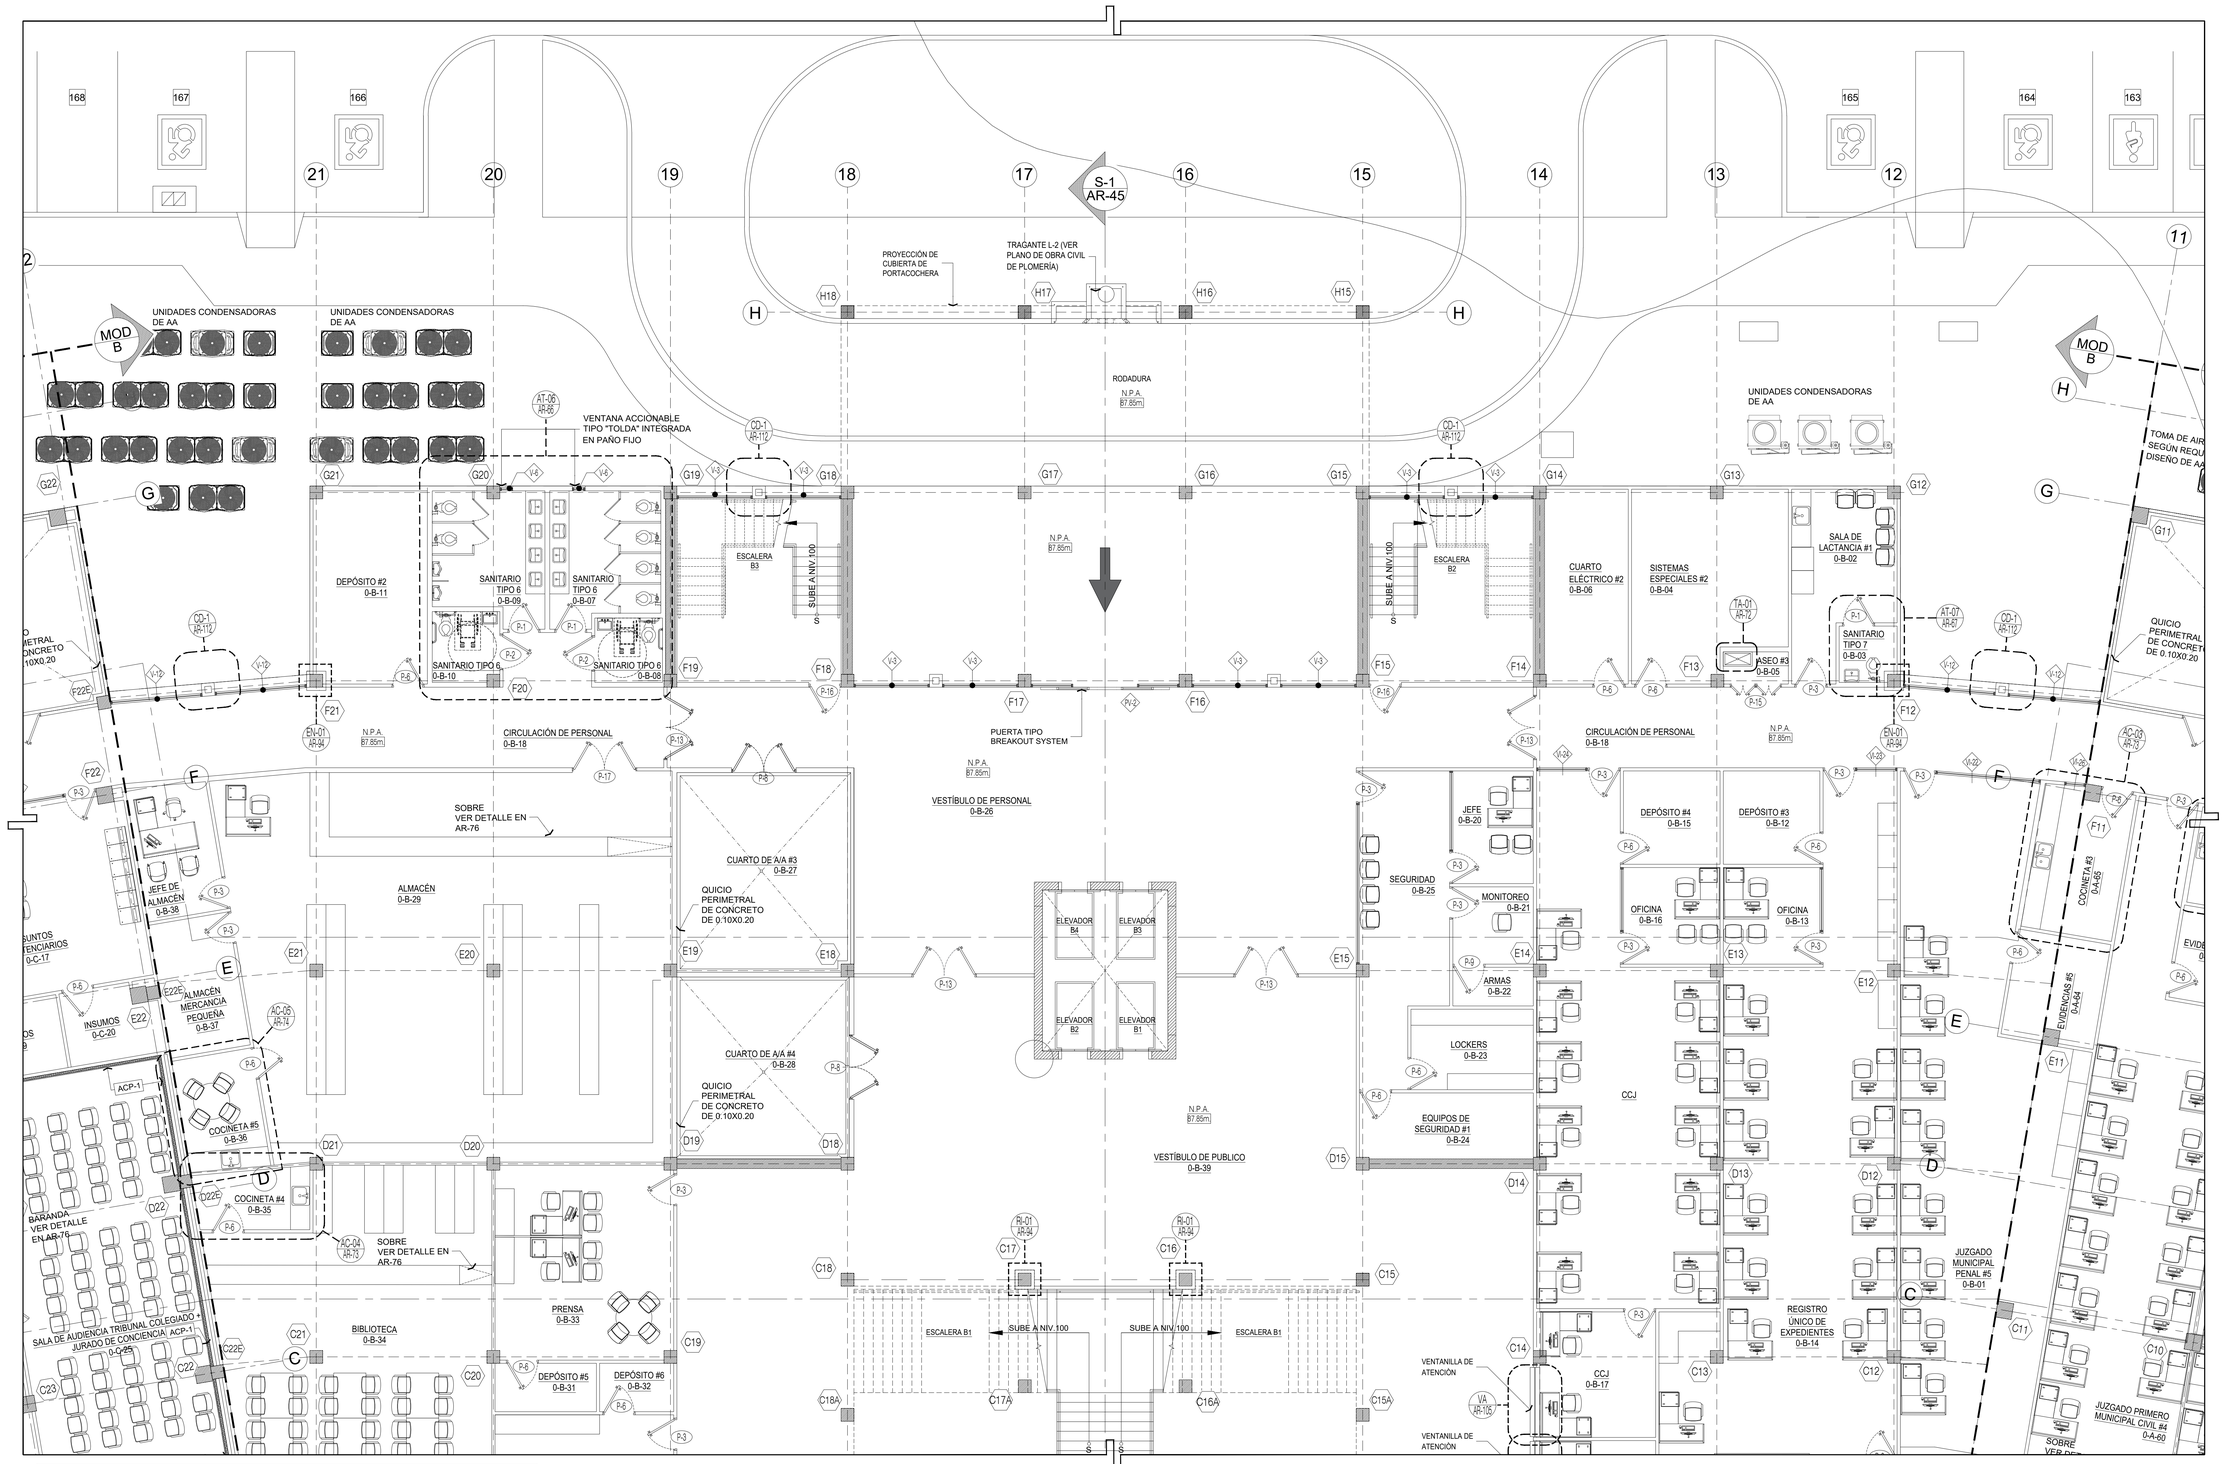

LEYENDA DE RECUBRIMIENTO DE COLUMNAS	
EN-01	ENCHAPE DE MORTERO DE CEMENTO REFORZADO + ACABADO EXTERIOR AC-4 (VER ELEVACIONES EN AR-46 @ AR-49)
RE-01	RECUBRIMIENTO EXTERIOR PARA COLUMNAS DE HORMIGÓN DE LÁMINAS DE FIBROCEMENTO DE 14mm + MORTERO CEMENTICIO PARA EXTERIORES DE 1.5mm + ACABADO DE MORTERO ACRÍLICO EXTRALISO + PINTURA 100% ACRÍLICA PARA EXTERIORES
RI-01	RECUBRIMIENTO PARA COLUMNAS DE HORMIGÓN DE LÁMINAS DE FIBROCEMENTO DE 14mm+ MORTERO CEMENTICIO DE 1.5mm + ACABADO DE MORTERO ACRÍLICO EXTRALISO + PINTURA 100% ACRÍLICA PARA INTERIORES

AMP-08 / AR-11

AMPLIACIÓN DE PLANTA AMOBLADA Y SIMBOLOGÍA NIVEL 000

ESC 1:75

MÓDULO B POSTERIOR

LEYENDA DE ACABADO DE PAREDES ACÚSTICAS	
ACP-1	PARED DE GYPSUM BOARD ACÚSTICO CON LÁMINAS DE LANA DE ROCA CON MICRÓFONOS OCULTOS.

NOTAS:
1. PARA EL ACABADO DE SANITARIOS Y COCINETAS VER AMPLIACIONES.
2. PARA EL RESTO DE LAS PAREDES VER CUADRO DE ACABADOS.

REPÚBLICA DE PANAMÁ
ÓRGANO JUDICIAL
SISTEMA PENAL ACUSATORIO PANAMÁ

REPRESENTANTE LEGAL O DUEÑO
CÉDULA:

C B A
CLAVE DE UBICACIÓN

PROYECTO:
EDIFICIO DE LA UNIDAD JUDICIAL REGIONAL DE PANAMÁ OESTE

PROPIETARIO:
ÓRGANO JUDICIAL

UBICACIÓN:
CORREGIMIENTO DE PLAYA LEONA, DISTRITO DE LA CHORRERA, PROV. DE PANAMÁ OESTE, REPÚBLICA DE PANAMÁ.

CONSORCIO RM - FÉMUR UNIDAD JUDICIAL
fémur — DISEÑA
RM — CONSTRUYE

APROBADO

DIRECTOR DE OBRAS Y CONSTRUCCIONES MUNICIPALES

DISEÑO GILBERTO GUARDIA N.	DIBUJO FEMUR
ESTRUCTURA ING. VICTOR CANO	ELECTRICIDAD ING. GABRIEL GARZON
ELECTRICIDAD ING. GABRIEL GARZON	PLOMERÍA ING. GABRIEL GARZON
PLANO No. 1	
FECHA MARZO 2023	ESCALA INDICADA

CONTENIDO DE LA HOJA
PLANTA AMOBLADA Y SIMBOLOGÍA NIVEL 000_MÓDULO B POSTERIOR

HOJA: AR-11 DE 127
PLANOS CONSTRUCTIVOS
TAM 12 X 420